Republika e Kosovës
Republika Kosova-Republic of Kosova
Qeveria -Vlada-Government

Ministria e Mjedisit dhe Planifikimit Hapësinor /Ministarstvo Sredine i Prostornog Planiranja/Ministry of Environment and Spatial Planning

AGJENCIA KADASTRALE E KOSOVËS/ KATASTARSKA AGECIJA KOSOVA/ KOSOVA CADASTRAL AGENCY

Zyra kadastrale komunale / Opštinska katastarska kancelarija: Ferizaj

Nr. i njësisë kadastrale / Br. katastarske jedinice : 288-0 290-2

Zona kadastrale / Katastarska zona: Jezerc

Numri i lëndës / Broj predmeta:

Lloji i njësisë kadastrale / Vrsta katastarske jedinice : Parcel

Shkalla e zvoglimit / Razmera plana : 1:750

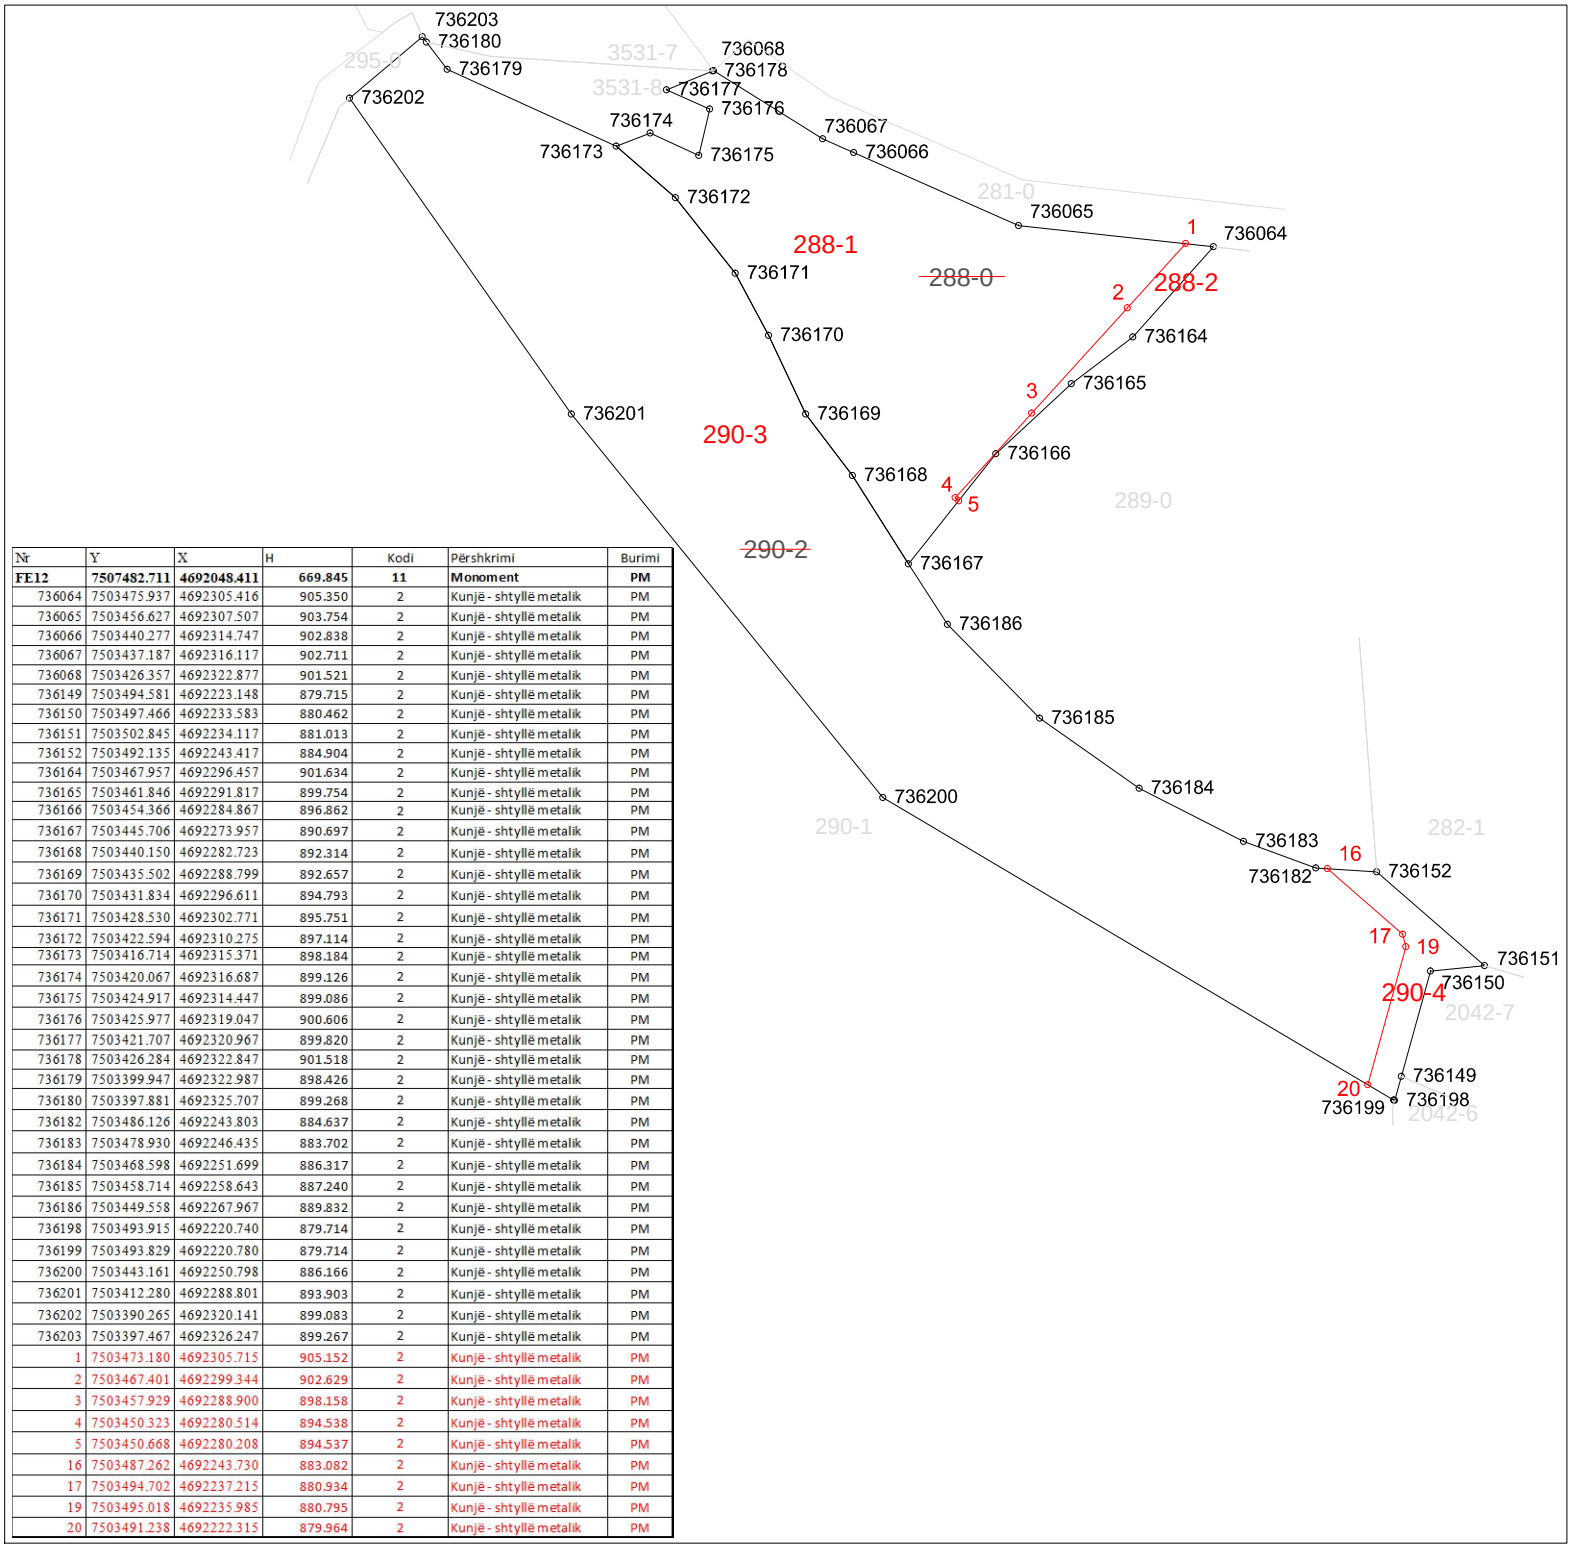

Nr	Y	X	H	Kodi	Përshkrimi	Burimi
FE12	**7507482.711**	**4692048.411**	**669.845**	**11**	**Monoment**	**PM**
736064	7503475.937	4692305.416	905.350	2	Kunjë - shtyllë metalik	PM
736065	7503456.627	4692307.507	903.754	2	Kunjë - shtyllë metalik	PM
736066	7503440.277	4692314.747	902.838	2	Kunjë - shtyllë metalik	PM
736067	7503437.187	4692316.117	902.711	2	Kunjë - shtyllë metalik	PM
736068	7503426.357	4692322.877	901.521	2	Kunjë - shtyllë metalik	PM
736149	7503494.581	4692223.148	879.715	2	Kunjë - shtyllë metalik	PM
736150	7503497.466	4692233.583	880.462	2	Kunjë - shtyllë metalik	PM
736151	7503502.845	4692234.117	881.013	2	Kunjë - shtyllë metalik	PM
736152	7503492.135	4692243.417	884.904	2	Kunjë - shtyllë metalik	PM
736164	7503467.957	4692296.457	901.634	2	Kunjë - shtyllë metalik	PM
736165	7503461.846	4692291.817	899.754	2	Kunjë - shtyllë metalik	PM
736166	7503454.366	4692284.867	896.862	2	Kunjë - shtyllë metalik	PM
736167	7503445.706	4692273.957	890.697	2	Kunjë - shtyllë metalik	PM
736168	7503440.150	4692282.723	892.314	2	Kunjë - shtyllë metalik	PM
736169	7503435.502	4692288.799	892.657	2	Kunjë - shtyllë metalik	PM
736170	7503431.834	4692296.611	894.793	2	Kunjë - shtyllë metalik	PM
736171	7503428.530	4692302.771	895.751	2	Kunjë - shtyllë metalik	PM
736172	7503422.594	4692310.275	897.114	2	Kunjë - shtyllë metalik	PM
736173	7503416.714	4692315.371	898.184	2	Kunjë - shtyllë metalik	PM
736174	7503420.067	4692316.687	899.126	2	Kunjë - shtyllë metalik	PM
736175	7503424.917	4692314.447	899.086	2	Kunjë - shtyllë metalik	PM
736176	7503425.977	4692319.047	900.606	2	Kunjë - shtyllë metalik	PM
736177	7503421.707	4692320.967	899.820	2	Kunjë - shtyllë metalik	PM
736178	7503426.284	4692322.847	901.518	2	Kunjë - shtyllë metalik	PM
736179	7503399.947	4692322.987	898.426	2	Kunjë - shtyllë metalik	PM
736180	7503397.881	4692325.707	899.268	2	Kunjë - shtyllë metalik	PM
736182	7503486.126	4692243.803	884.637	2	Kunjë - shtyllë metalik	PM
736183	7503478.930	4692246.435	883.702	2	Kunjë - shtyllë metalik	PM
736184	7503468.598	4692251.699	886.317	2	Kunjë - shtyllë metalik	PM
736185	7503458.714	4692258.643	887.240	2	Kunjë - shtyllë metalik	PM
736186	7503449.558	4692267.967	889.832	2	Kunjë - shtyllë metalik	PM
736198	7503493.915	4692220.740	879.714	2	Kunjë - shtyllë metalik	PM
736199	7503493.829	4692220.780	879.714	2	Kunjë - shtyllë metalik	PM
736200	7503443.161	4692250.798	886.166	2	Kunjë - shtyllë metalik	PM
736201	7503412.280	4692288.801	893.903	2	Kunjë - shtyllë metalik	PM
736202	7503390.265	4692320.141	899.083	2	Kunjë - shtyllë metalik	PM
736203	7503397.467	4692326.247	899.267	2	Kunjë - shtyllë metalik	PM
1	7503473.180	4692305.715	905.152	2	Kunjë - shtyllë metalik	PM
2	7503467.401	4692299.344	902.629	2	Kunjë - shtyllë metalik	PM
3	7503457.929	4692288.900	898.158	2	Kunjë - shtyllë metalik	PM
4	7503450.323	4692280.514	894.538	2	Kunjë - shtyllë metalik	PM
5	7503450.668	4692280.208	894.537	2	Kunjë - shtyllë metalik	PM
16	7503487.262	4692243.730	883.082	2	Kunjë - shtyllë metalik	PM
17	7503494.702	4692237.215	880.934	2	Kunjë - shtyllë metalik	PM
19	7503495.018	4692235.985	880.795	2	Kunjë - shtyllë metalik	PM
20	7503491.238	4692222.315	879.964	2	Kunjë - shtyllë metalik	PM

Rilevoi / Snimio: SEAD PRUSHI
(emri dhe mbiemri i gjeodetit/kompanisë/ ime i prezime geodeta/ kompanije)

Aprovoi / Usvojio: _____
(emri dhe mbiemri i përsonit zyrtar/ ime i prezime sluzbenog lica)

Nr. i licencës / Br. licence: 152

V.V.

Nënshkrimi / Potpis: _____

Nënshkrimi / Potpis: _____

Data e rilevimit / Datum snimanja: 08.07.2020

Data e aprovimit / Datum usvajanja: _____